

Existing Key Legend

As Provided Client Existing Fire Plan Drawing
MHB-TEN-3-16001-R12 - Issue Date:29.06.2009

- Atria Enclosure (smoke retarding construction)
- 30 Min Fire Resisting - Hazard Rooms and Protected Corridors
- 30 Min Fire Resisting Sub-compartment Wall
- 60 Min Fire Resisting Compartment Wall (1)
- 120 Min Fire Resisting Wall

Allowance to be made for appropriate horizontal fire-stopping to be applied to the roof at the head of ALL newly positioned compartment walls (not sub-compartment walls); minimum 1500mm either side of the wall. Use of approved product/materials to current British Standards.

NOTES
All dimensions and levels to be checked on site
Any discrepancies are to be reported to the Architect before any work commences
This drawing shall not be scaled to ascertain any dimensions, work to figured dimensions only
This drawing shall not be reproduced without express written permission from AFL Architects Ltd
DISCLAIMER
When this drawing is issued in CAD, it is an uncontrolled version issued for information only, to enable the recipient to prepare their own documents/drawings for which they are solely responsible.
SOFTWARE INTEROPERABILITY
AFL prepared this drawing using Autodesk REVIT Architecture.
AFL does not accept liability for any loss or degradation of any information held in the drawing resulting from the translation from the original file format to any other file format or from the recipients reading of it in any other programme.


General Note:

This is a colour drawing
60min Fire protection to columns
Limited to Number of sprinkler heads in each zone T.B.C on site otherwise 90min Fire protection to columns required.

Site survey of external wall windows heights required by other to determine HTM-05-02 Unprotected area.

Fire dampers to be placed in proposed new shaft wall rather than existing wall if required

Please allow for remedial works to any existing walls in relation to any fire upgrades

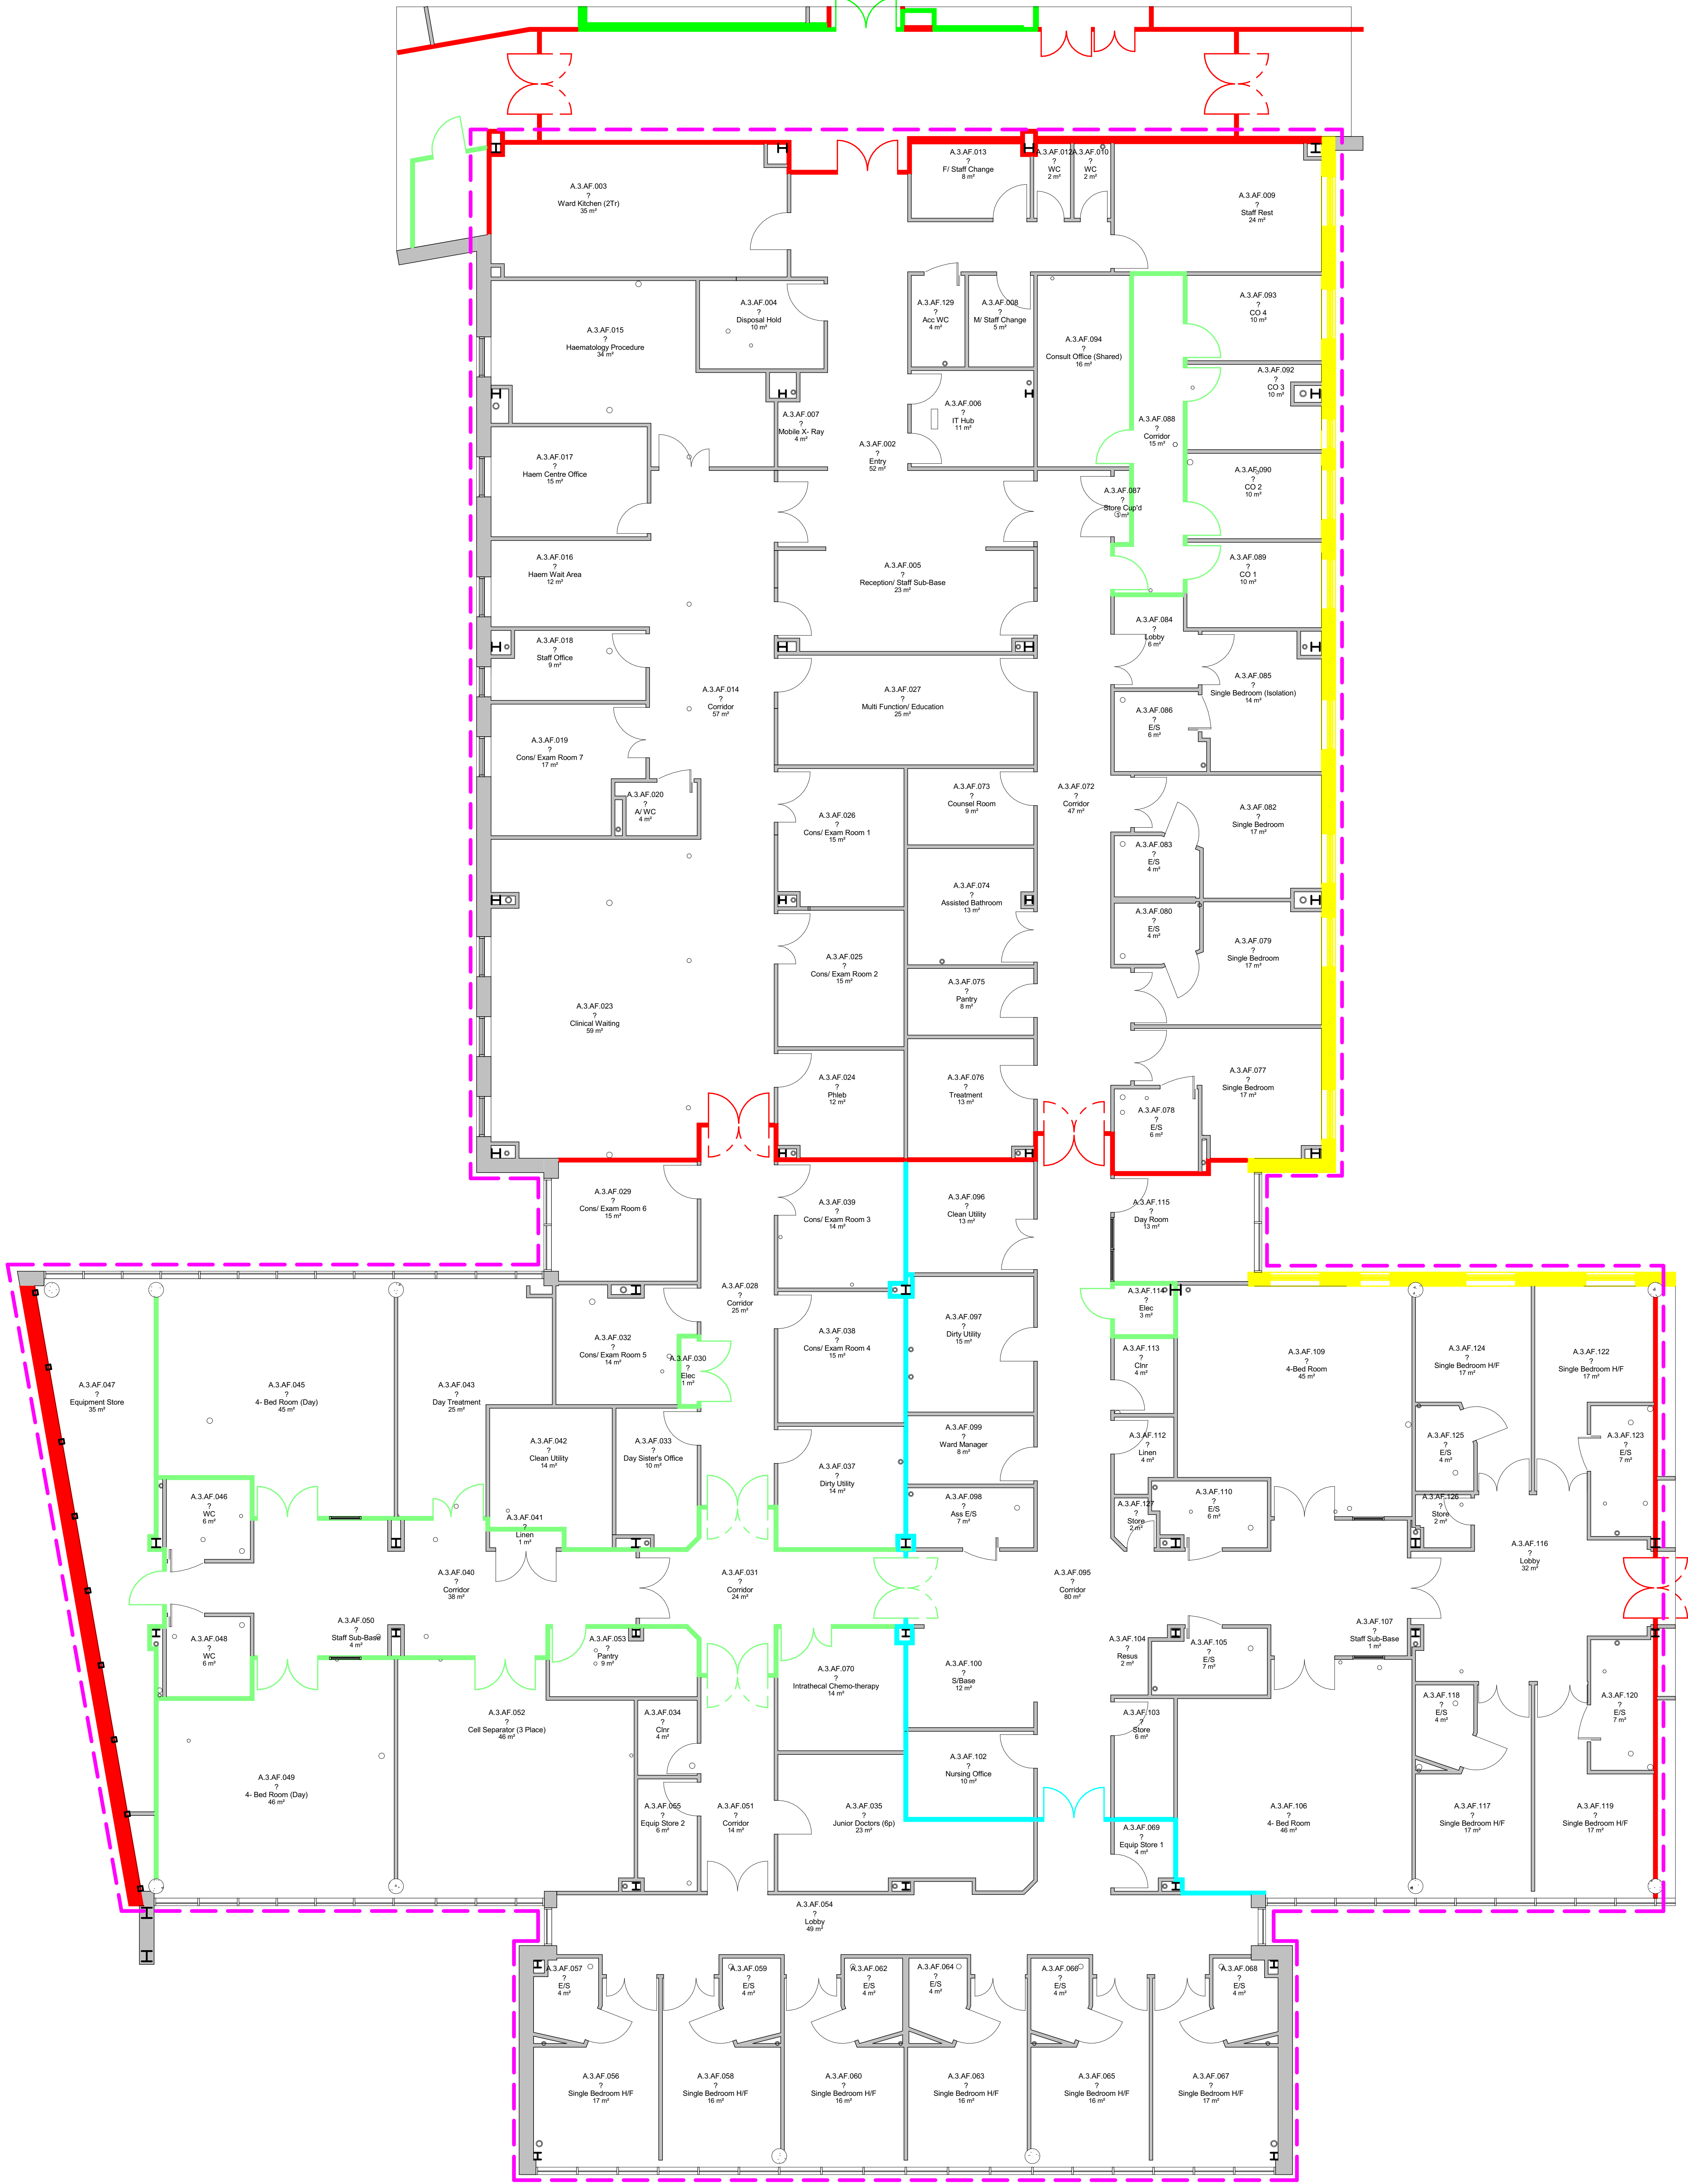

rev	no	date	rev by	description
1	1	19.05.17	15	TENDER ISSUE

project

MRL_Ward 44 BMTU

location

K50/03

Employer

client

Central Manchester University
Hospitals NHS Foundation Trust



AFL Architects
1st Floor
56 George Street
56 Peter Street
Manchester, M2 3JQ

T: +44(0)161 236 6263
F: +44(0)161 236 6484

www.aflarchitects.com
e: mail@afl-uk.com

twitter.com/AFLArchitects
key plan

drawing title

Existing Fire Plan

AFL job number	scale	@ A0	drawn	PPS	checked	NP
163174	As Indicated					

draw purpose	status	rev
tender	D2	T 1

K5002-AFL-XX-03-DR-A-67100