


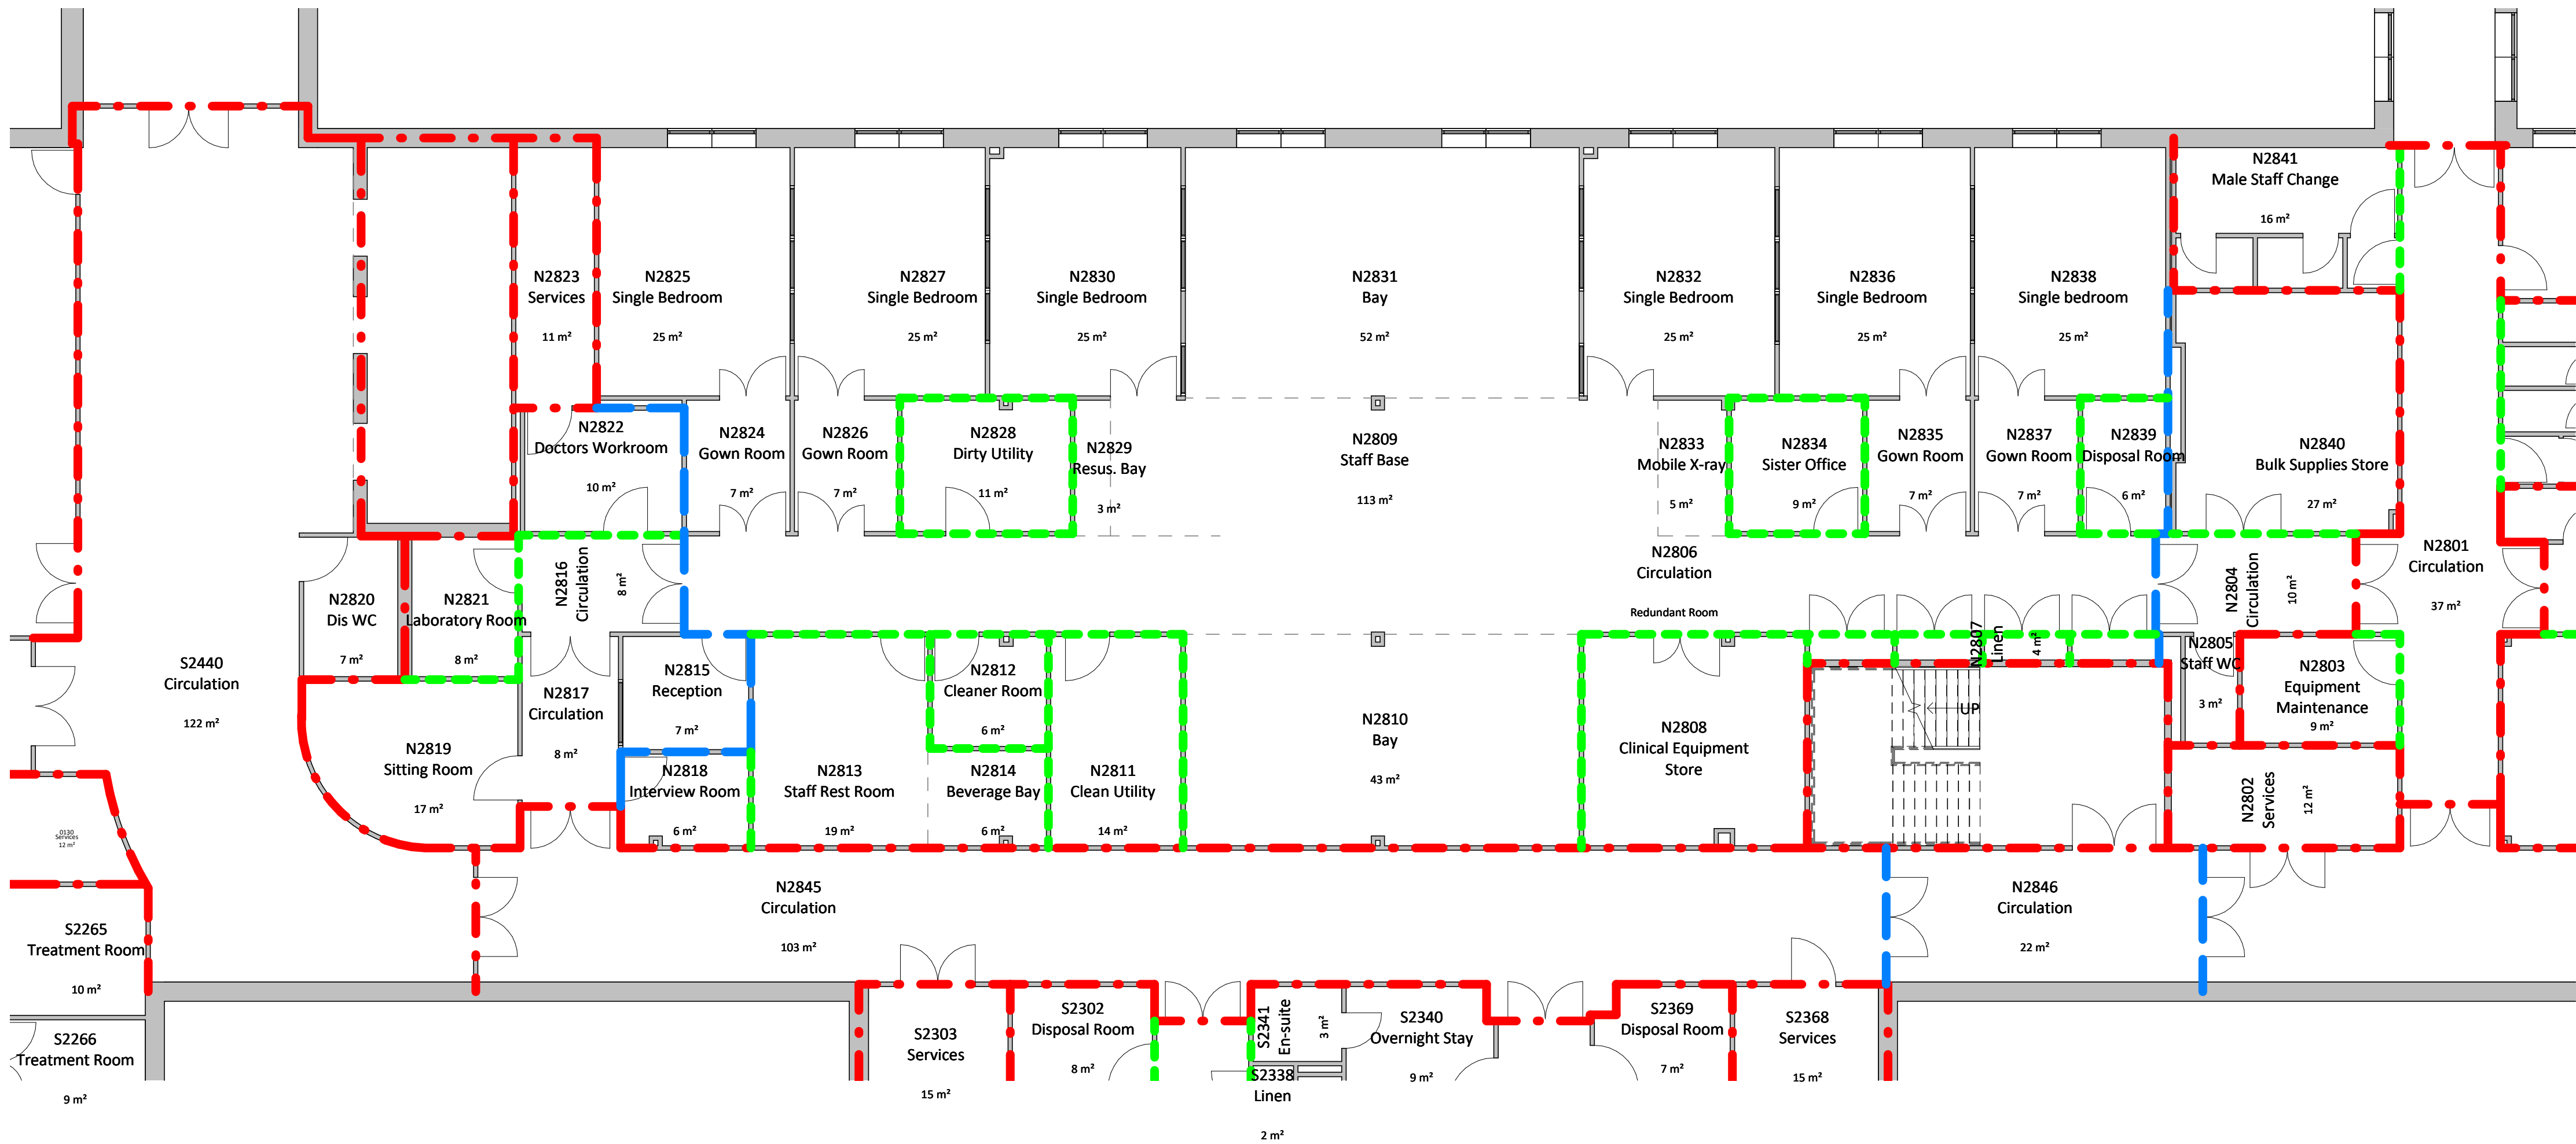

Existing Fire Plan - Ward A

1 : 100



Existing Fire Plan - Ward B

1 : 100

Fire Plan Legend

- 60-minute fire-resistant compartment walls
- 30-minute fire-resistant sub-compartment walls / fire risk rooms
- Fire-rated walls / compartmentation - unknown

Fire strategy based upon unutilised Fire plan provided by Engie - Stephen Sedgwick

NOTES

All dimensions and levels to be checked on site

Any discrepancies are to be reported to the Architect before any work commences

This drawing shall not be scaled to ascertain any dimensions, work to figured dimensions only

This drawing shall not be reproduced without express written permission from AFL Architects Ltd.

DISCLAIMER

When this drawing is issued in CAD, it is an uncontrolled version issued for information only, to enable the recipient to prepare their own documents/drawings for which they are solely responsible.

SOFTWARE INTEROPERABILITY

AFL prepared this drawing using Autodesk REVIT Architecture.

AFL does not accept liability for any loss or degradation of any information held in the drawing resulting from the translation from the original file format to any other file format or from the recipients reading of it in any other programme.

P 1 18.05.18 JS First Issue

rev no.	rev date	rev by	description
---------	----------	--------	-------------

project

Critical Care Lifecycle

location

Royal Blackburn Hospital

Employer



client

Engie

AFL Architects

1st Floor
St Georges House
56 Peter Street
Manchester UK
M2 3NQ

t: +44(0)161 236 6263

f: +44(0)161 236 6484

w: www.afl-architects.com

e: mail@afl-uk.com

twitter.com/AFLArchitects

key plan



drawing title

Existing Fire Plan

AFL job number scale @ A1 drawn JS checked NP

183163 As indicated rev date 18.05.18

dwg purpose	status	rev
Preliminary	S2	P 1

bim project origin zone level type role 5-digit no.

183163-AFL-00-02-DR-A-67101